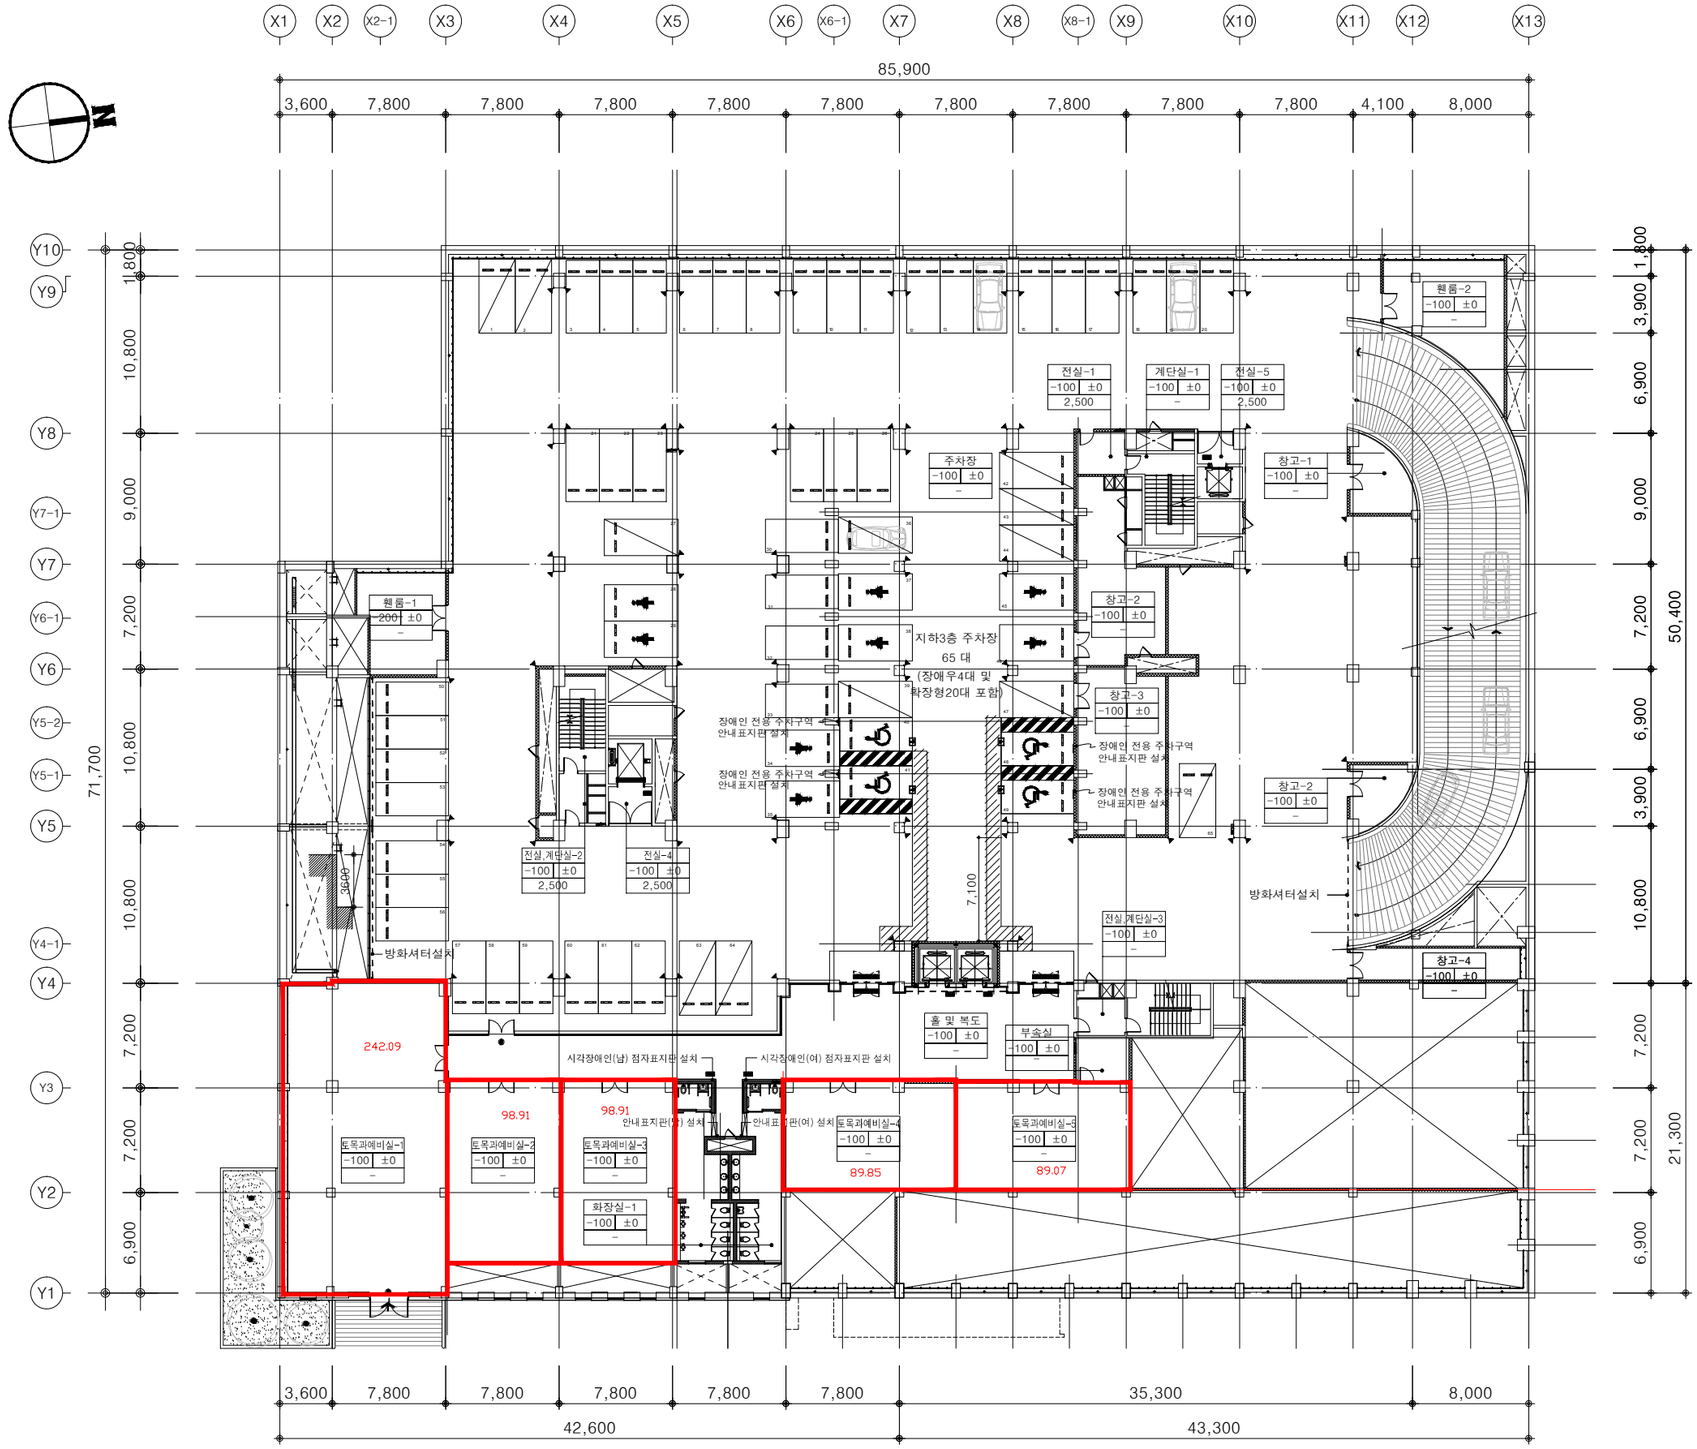


1 지하3층 평면도

축척 : 1 / 400

(주)엔씨티엔지니어링
종합건축사사무소
경기도 화성시 병점동 844-2
탑프라자 605호
TEL (031) 898-5481
FAX (031) 898-5437

■NOTE

1. 지하3층 FL±0 = E.L. +35.30
2. 주요마감재 시공시 현장실측 후 공종별 SHOP DWG를 작성하여 감리자 및 감독관의 승인을 득한 후 시공할 것.
3. 설계 사양 변경시 필히 감리자 및 감독관의 승인을 득한 후 시공할 것.
4. 이질재료 연결부는 재료분리대를 설치할 것. (THK1.5 SST.헤어라인,W=40)
5. 비내력 벽체는 THK.200 ALC블럭임
6. 갑종방화문 : ●
7. 완강기 : ㊊
8. 장애우 경고블럭: ▬

No.	Date	Revision Description	Chkd.
△			
△			
△			

설계명 Project: 수원대학교 이공과대학 강의동

승인 Approved: 오 정 준

설계 Architect: 정 순 철

검토 Chkd:

담당 Drawn:

도면명 Title: 지하3층 평면도

축척 Scale: A1:1/200 A3:1/400

프로젝트번호 Project No.: 201400

도면번호 Drawing No.: A - 302

일련번호 Sheet No.: Rev. No. △