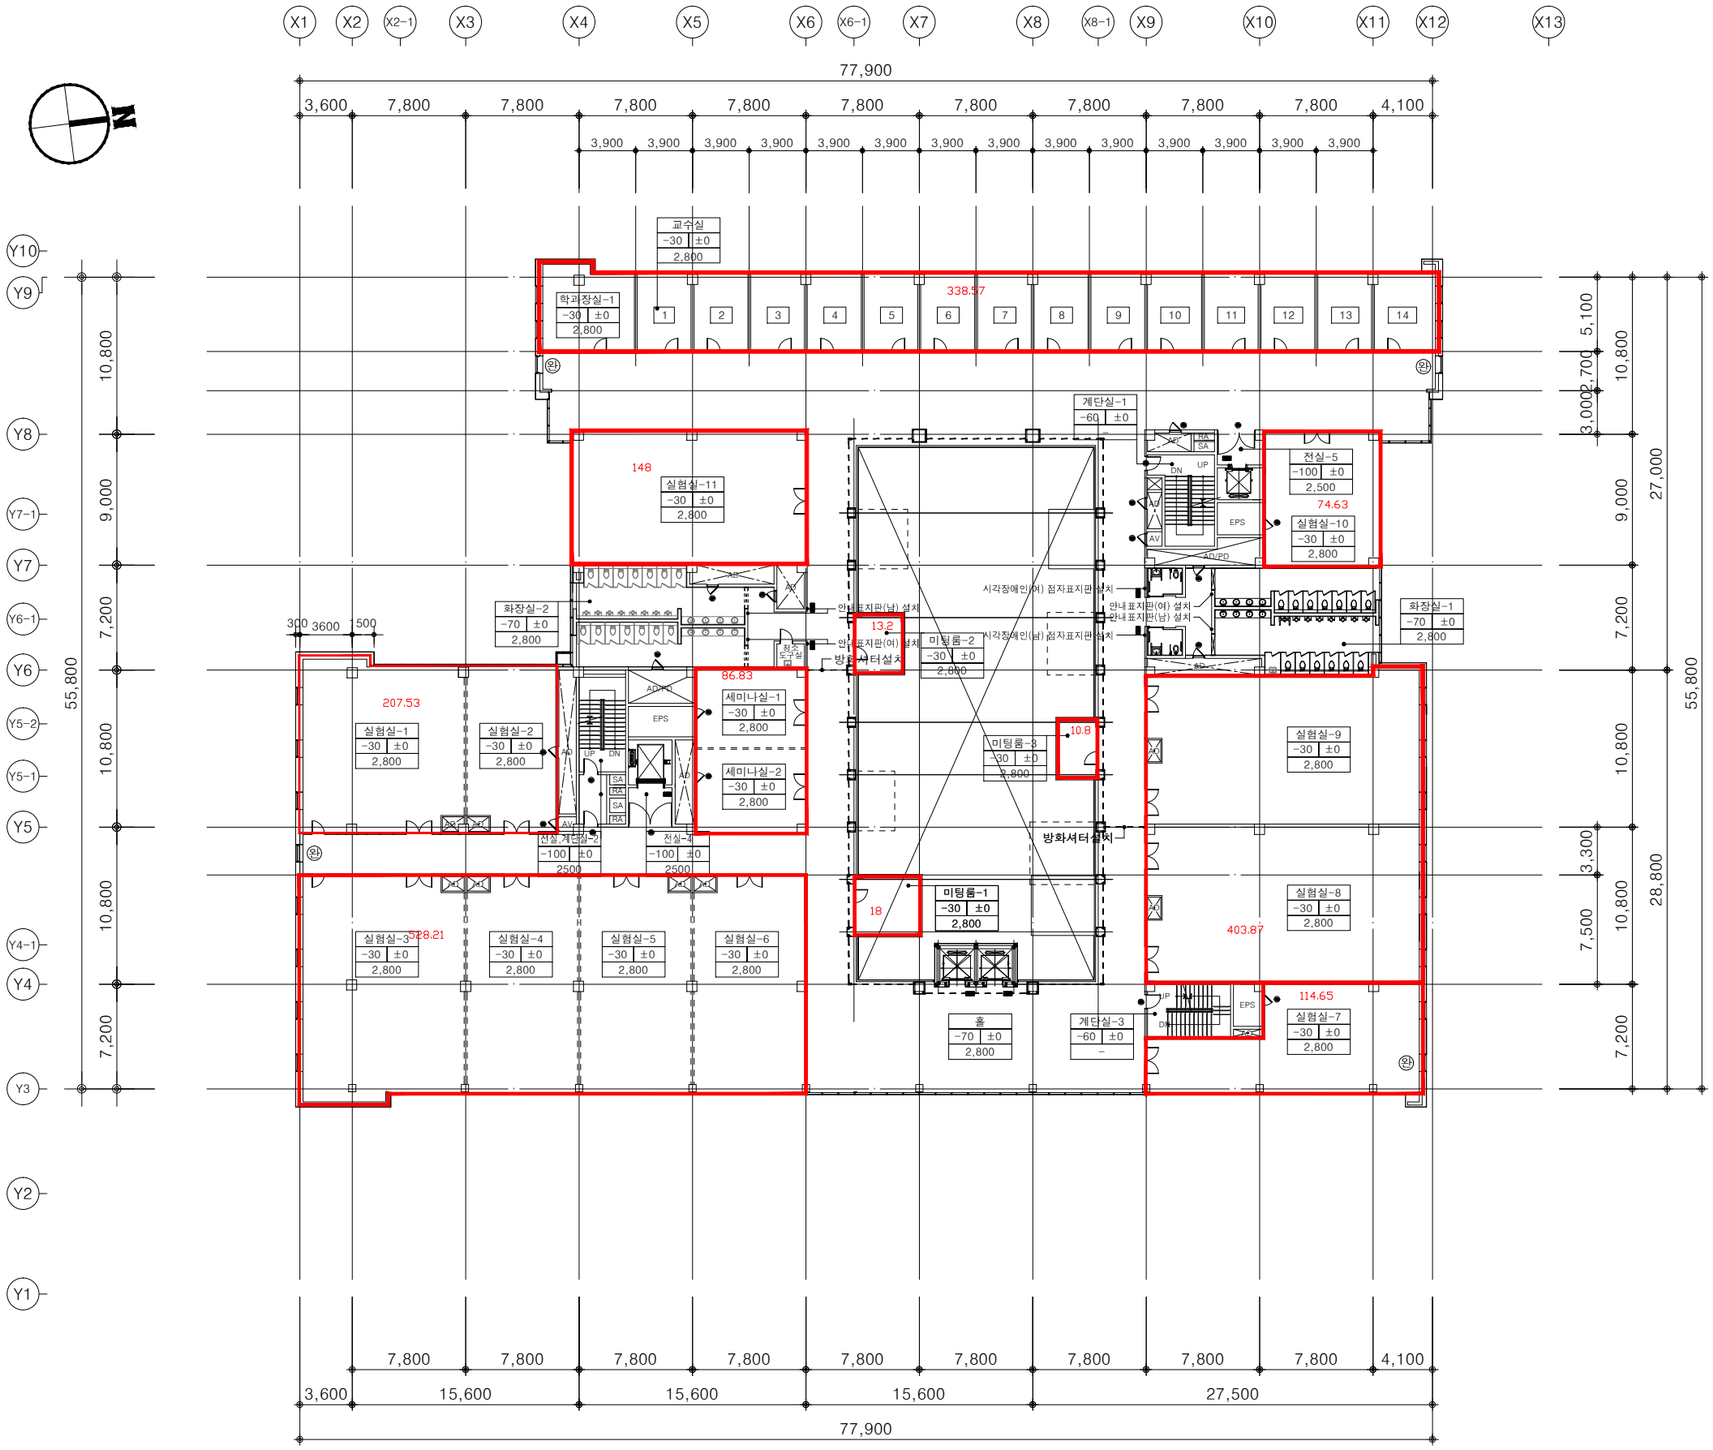


1 지상6층 평면도

축척 : 1 / 400

(주)엔씨티엔지니어링
종합건축사사무소
경기도 화성시 병점동 844-2
탑프라자 605호
TEL (031) 898-5481
FAX (031) 898-5437

■NOTE

1. 지상5층 FL±0 = E.L. +66.60
2. 주요마감재 시공시 현장실측 후 공종별 SHOP DWG를 작성하여 감리자 및 감독관의 승인을 득한 후 시공할 것.
3. 설계 사양 변경시 필히 감리자 및 감독관의 승인을 득한 후 시공할 것.
4. 이질재료 연결부는 재료분리대를 설치할 것. (THK1.5 SST.헤어라인,W=40)
5. 비내력 벽체는 THK.200 ALC블럭임
6. 갑종방화문 : ●
7. 완강기 : ㊍
8. 장애우 경고블럭: ▬
9. 내부 브라인더설치 :

No.	Date	Revision Description	Chkd.
△			
△			
△			

설계명 Project: 수원대학교 이공과대학 강의동

승인 Approved	오 정 준
설계 Architect	정 순 철
검토 Chkd	
담당 Drawn	

도면명 Title: 지상6층 평면도

축척 Scale	A1:1/200 A3:1/400
프로젝트번호 Project No.	201400
도면번호 Drawing No.	A-310
일련번호 Sheet No.	Rev. No. △