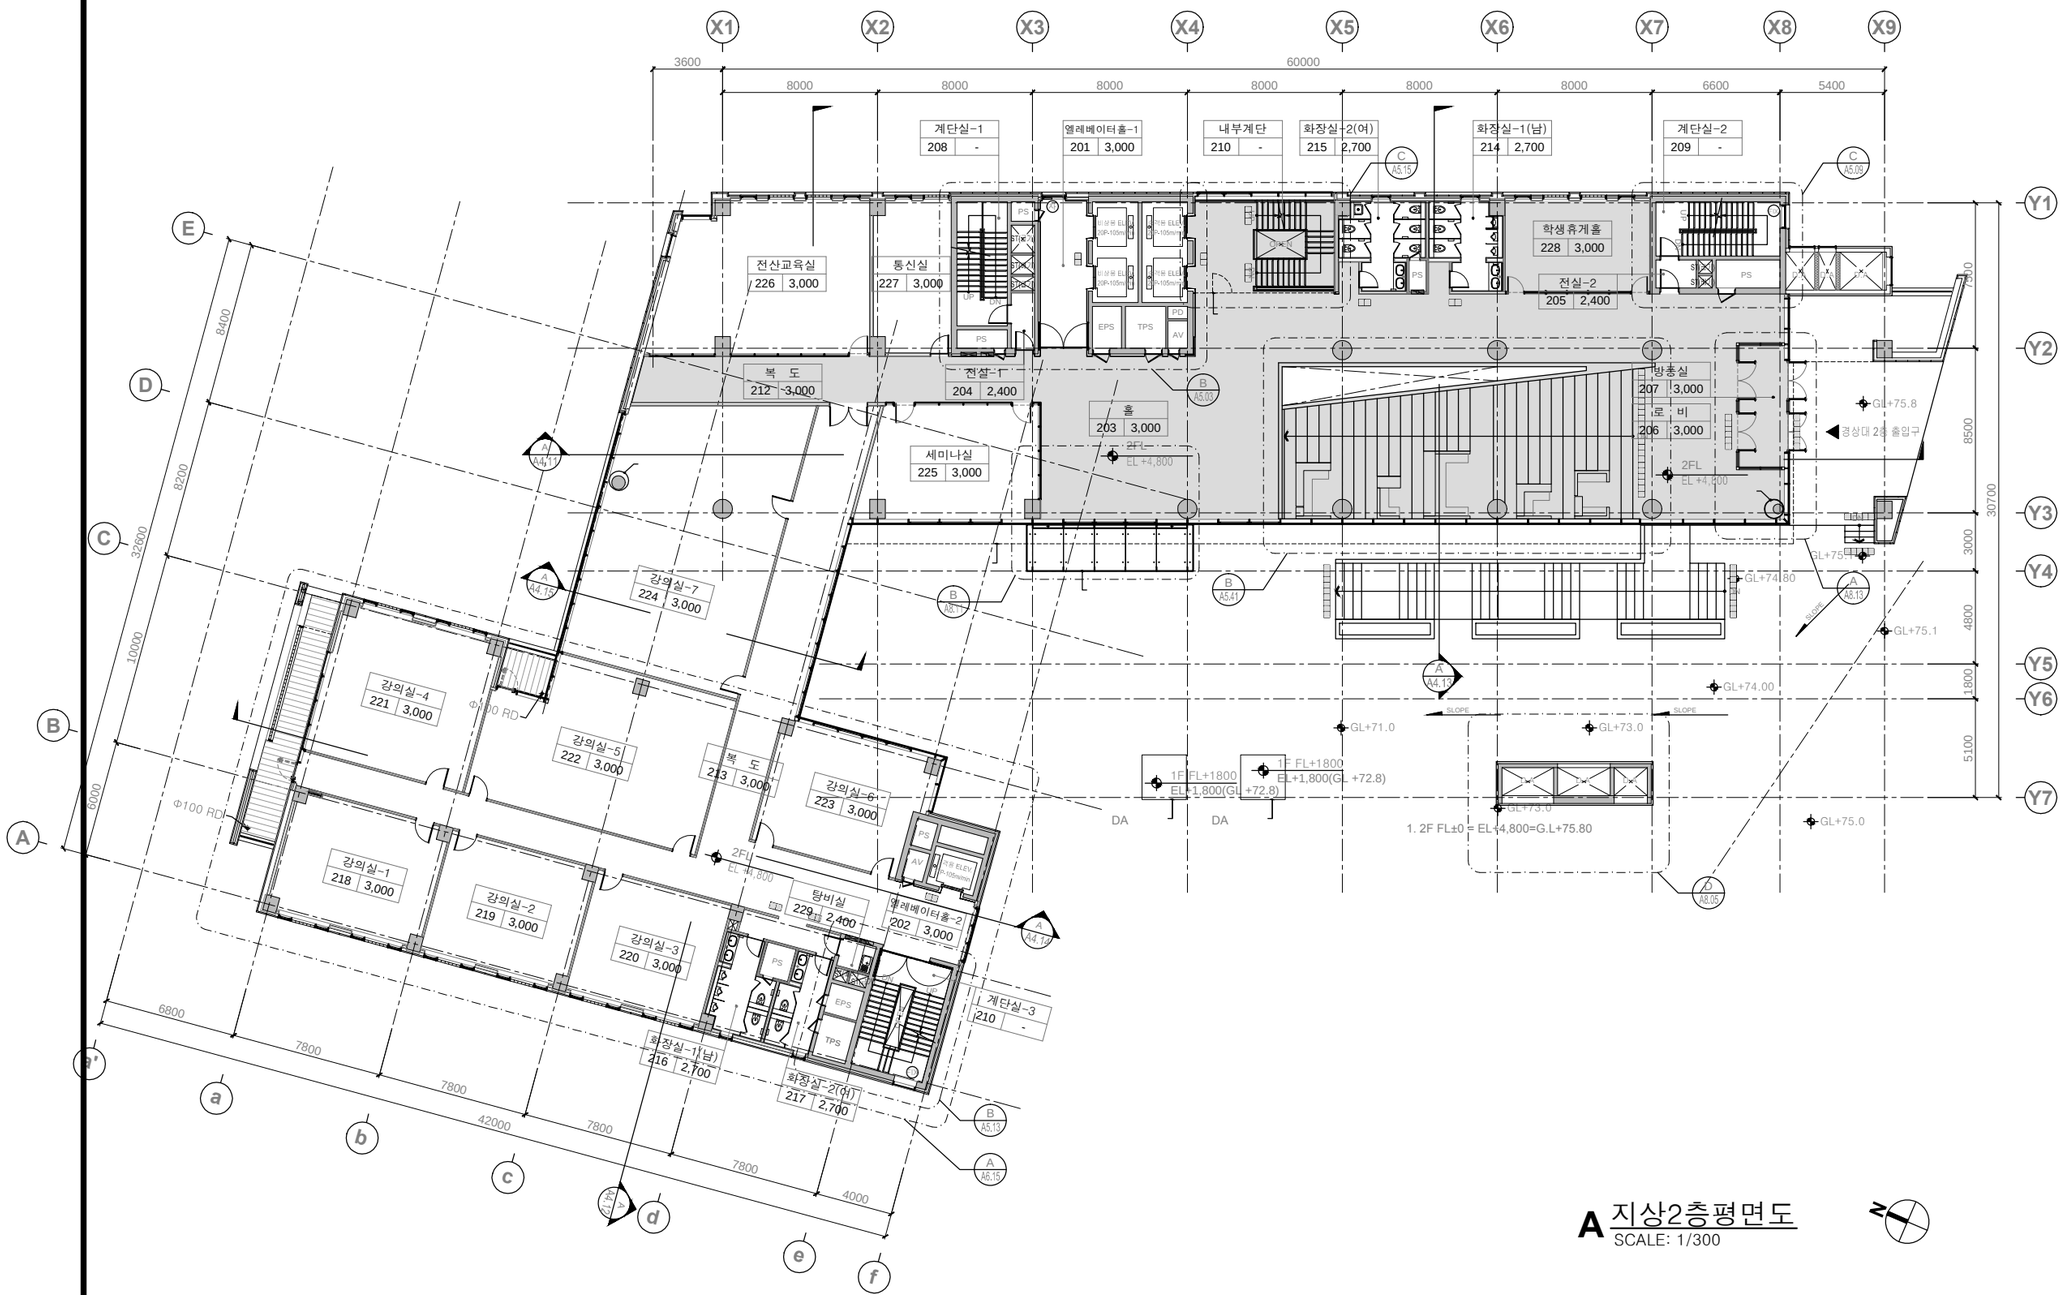



A 지상2층평면도
SCALE: 1/300

CLIENT
USW 수원대학교 THE UNIVERSITY OF SUWON

ARCHITECT
Chang-jo ARCHITECTS
(주)창조종합건축사사무소
826-26, Yeoksam-Dong,
Gangnam-Gu,Seoul,Korea 135-935
TEL. (82-2)2177-8300

PROJECT NO.
75241

PROJECT TITLE
수원대학교 경상대학 COMPLEX 증축설계

NOTE
1. 2F FL±0 = EL+4,800=G.L+75.80
2. 인테리어 영역

- 철골구조에 내화뿜칠 또는 내화페인트 적용기준: 2시간
- 13층 복층형 기숙사: 내화페인트
- 그외 철골구조: 내화뿜칠

| | |
|---|---|
| SP | 완 강 기 |
| | 옥내 소화전함 |
| | 방수기구함 |

| NO. | DESCRIPTION | | | DATE |
|---|---|---|---|---|
| 1 | 설계변경 수정사항 | | | 2015.06.30 |
| | 정현돈 | 최현 | 김경훈 | 이강우 |
| | DRAWN | CHECK 1 | | APPR |

ISSUES & REVISIONS

DRAWING TITLE
지상2층 평면도

| | | | |
|---|---|---|---|
| DRAWN | 한만수 | SCALE | A1 : 150<br>A3 : 300 |
| CHECK 1 | 김경훈 | | |
| CHECK 2 | 김영관 | DATE | 2013.11. |
| APPROVAL | 이강우 | | |

DRAWING NO.
A3-05