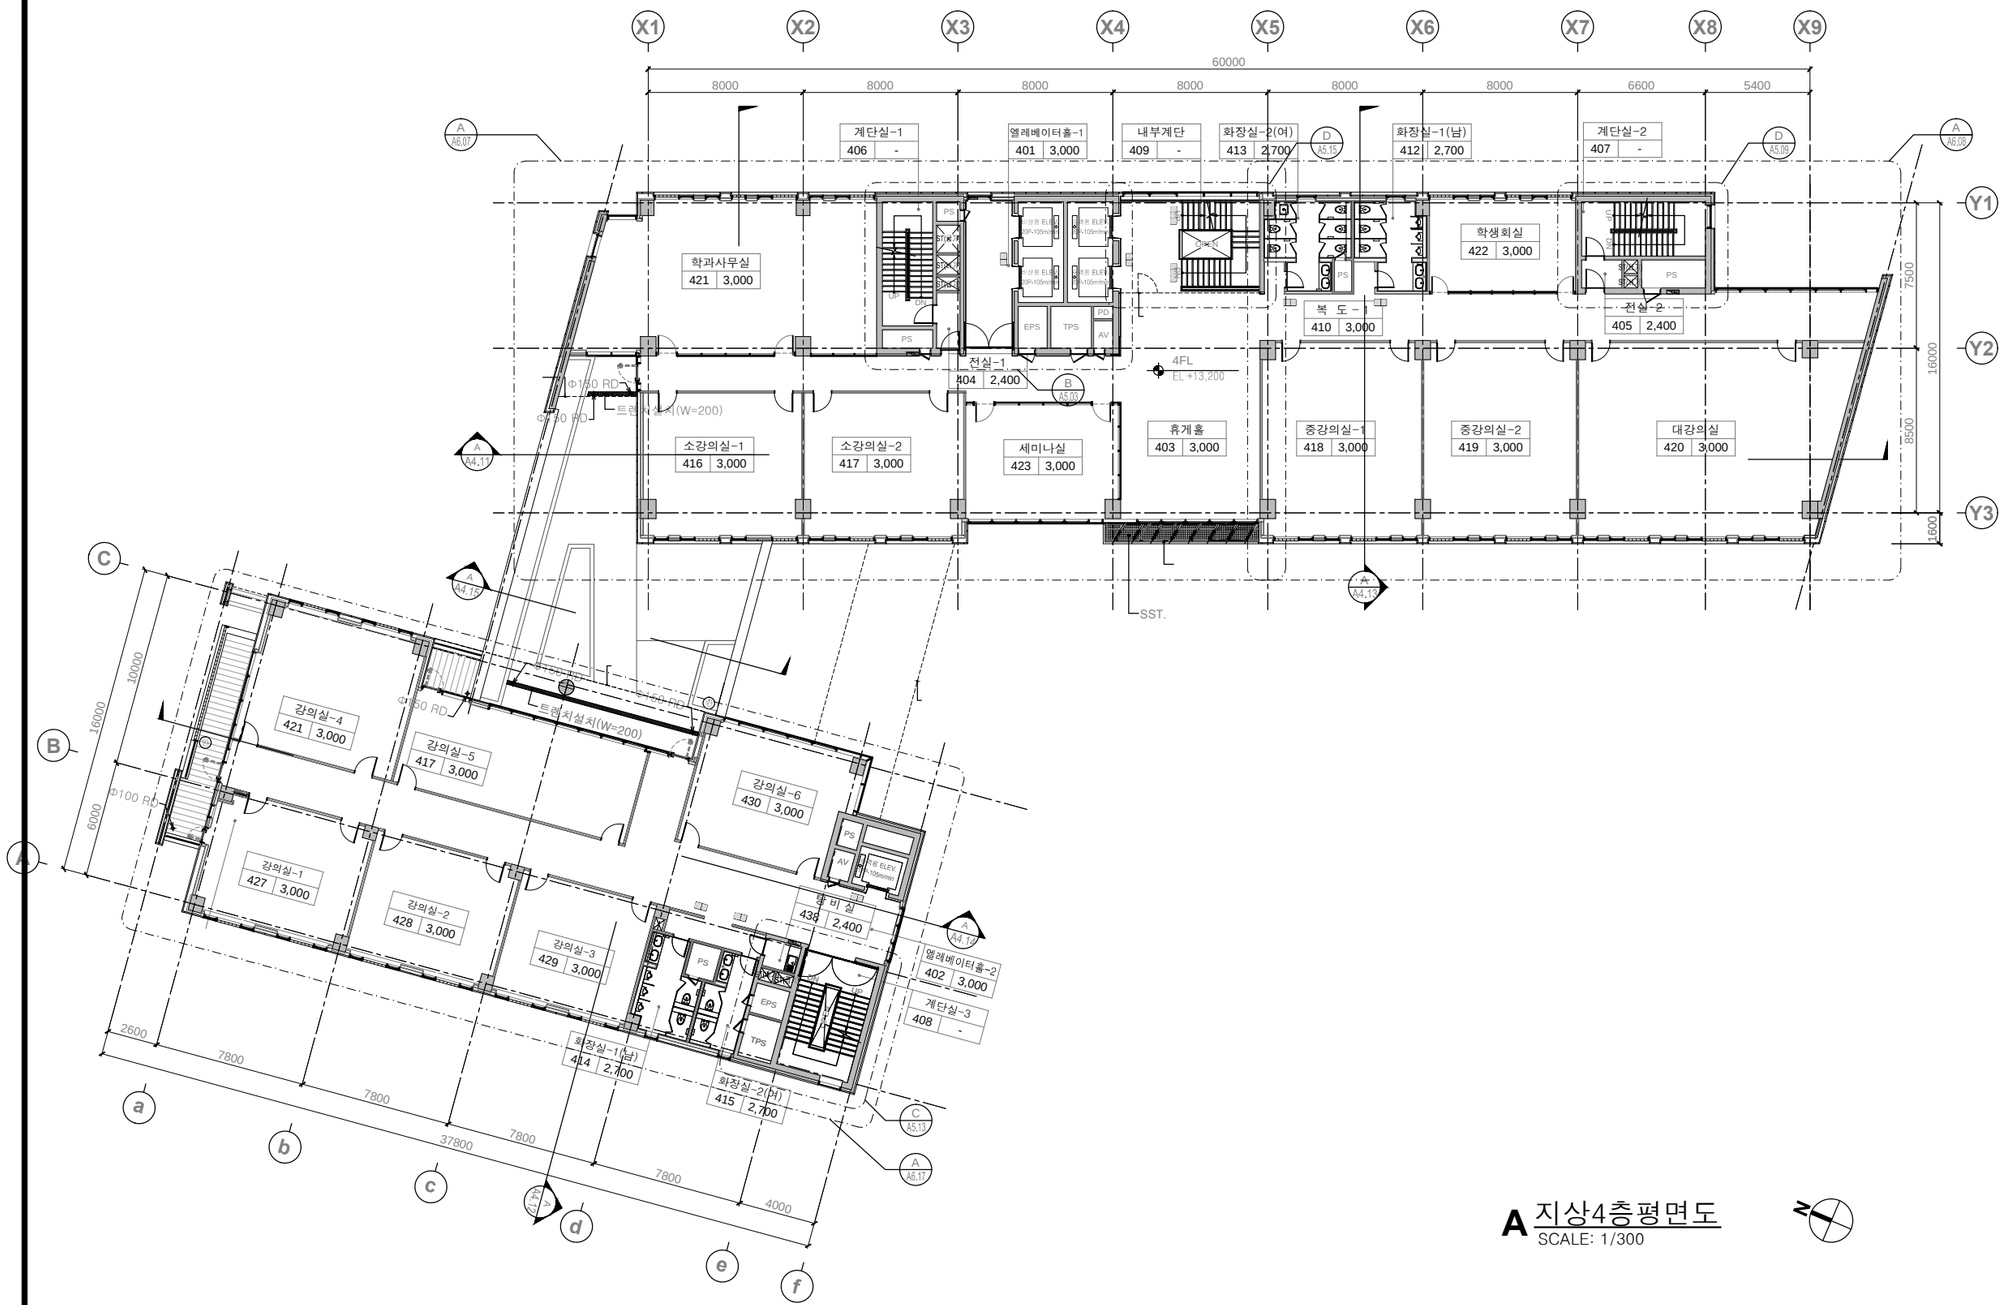


A 지상4층평면도
SCALE: 1/300

CLIENT

수원대학교
THE UNIVERSITY OF SUWON

ARCHITECT

Chang-jo
ARCHITECTS
(주)창조종합건축사사무소
826-26, Yeoksam-Dong,
Gangnam-Gu,Seoul,Korea 135-935
TEL. (82-2)2177-8300

PROJECT NO.

75241

PROJECT TITLE

수원대학교 경상대학 COMPLEX 증축설계

NOTE

1. 4F FL±0 = EL+13,200=G.L+84.20

- 철골구조에 내화뿜칠 또는 내화페인트 적용기준: 2시간
- 13층 복층형 기숙사: 내화페인트
- 그외 철골구조: 내화뿜칠

완 강 기	
옥내 소화전함	
방수기구함	

NO.	DESCRIPTION			DATE
1	설계변경 수정사항			2015.06.30
	정현돈	최현	김경훈	이강우
	DRAWN	CHECK 1		APPR

ISSUES & REVISIONS

DRAWING TITLE

지상4층 평면도

DRAWN	한만수	SCALE	A1 : 150 A3 : 300
CHECK 1	김경훈		
CHECK 2	김영관	DATE	2013.11.
APPROVAL	이강우		

DRAWING NO.

A3-07