
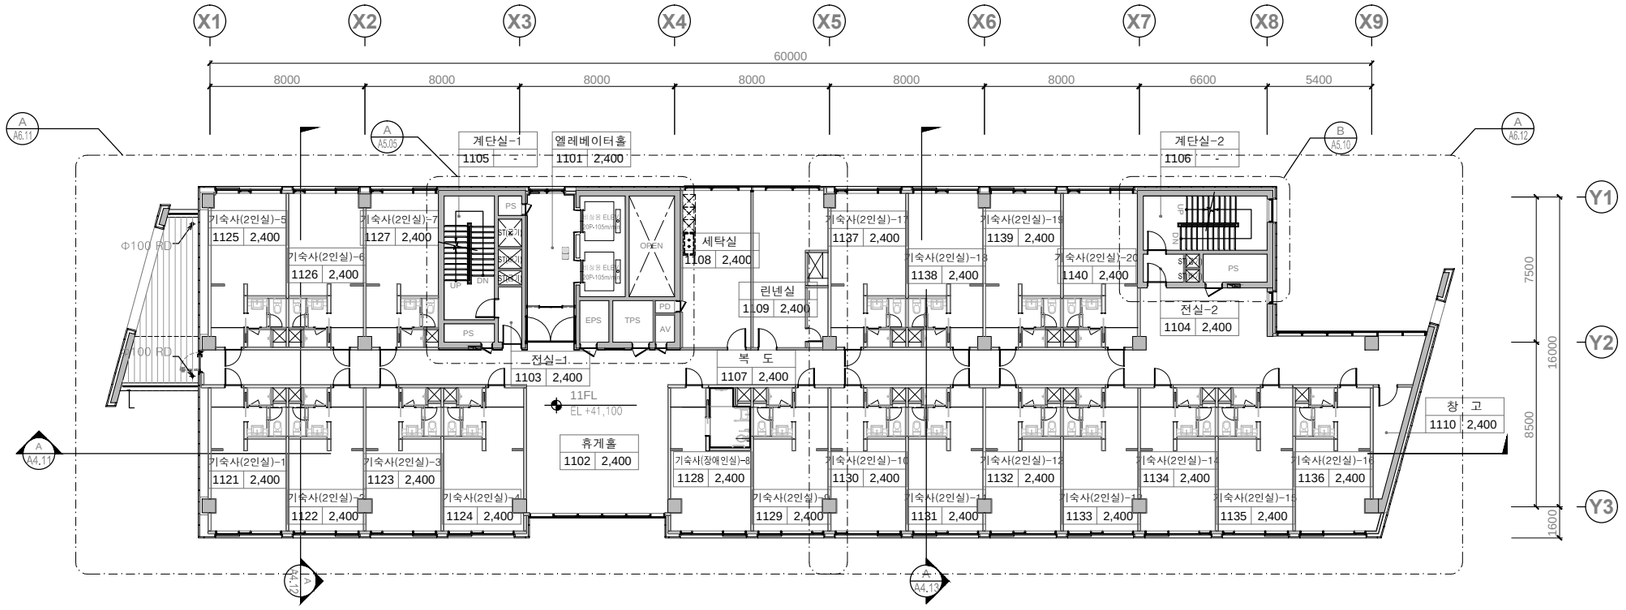


A 지상11층평면도
SCALE: 1/300

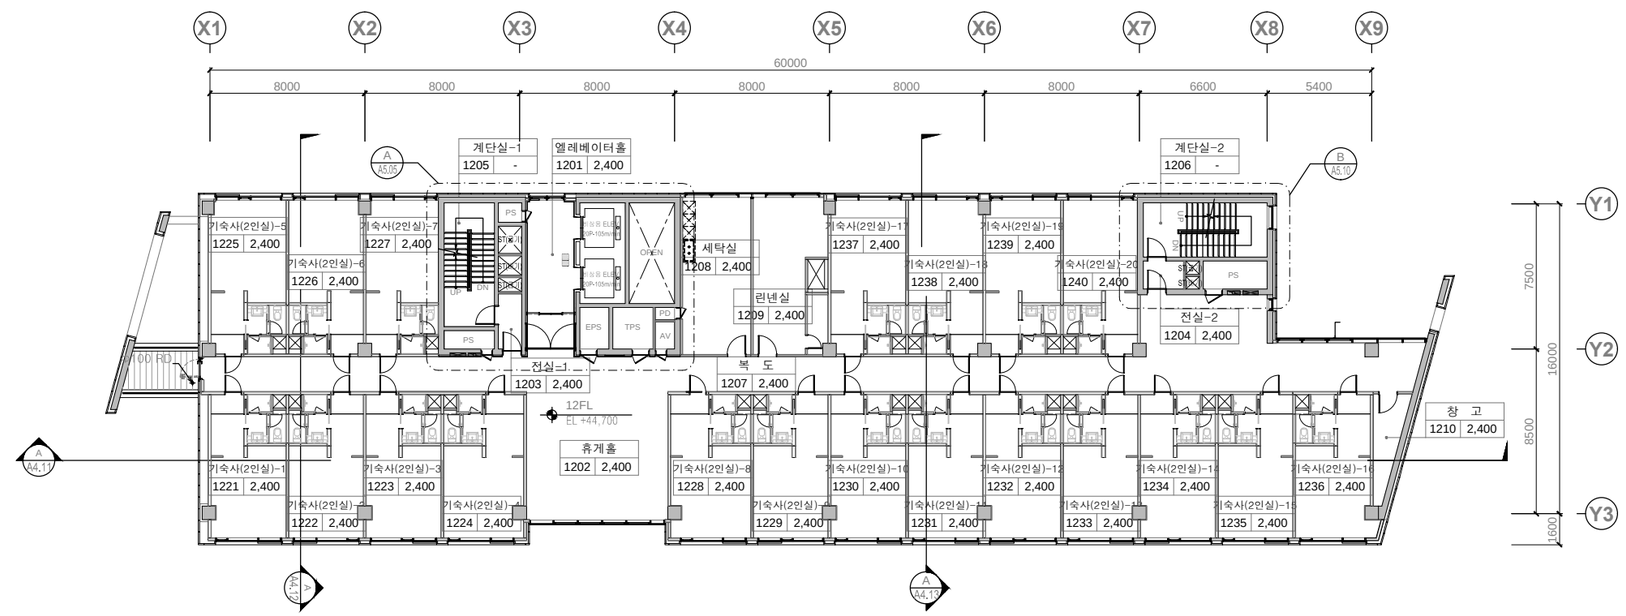

B 지상12층평면도
SCALE: 1/300

CLIENT
USW 수원대학교 THE UNIVERSITY OF SUWON

ARCHITECT
Chang-jo ARCHITECTS
(주)창조종합건축사사무소
826-26, Yeoksam-Dong,
Gangnam-Gu,Seoul,Korea 135-935
TEL. (82-2)2177-8300

PROJECT NO.
75241

PROJECT TITLE
수원대학교 경상대학 COMPLEX 증축설계

NOTE
1. 11F FL±0 = EL+41,100=G.L+112.10
2. 12F FL±0 = EL+44,700=G.L+115.70

*철골구조에 내화뿜칠 또는 내화페인트
적용기준: 2시간
13층 복층형 기숙사: 내화페인트
그외 철골구조: 내화뿜칠

옥내 소화전함
방수기구함

NO.	DESCRIPTION			DATE
1	설계변경 수정사항			2015.06.30
	정현돈	최현	김경훈	이강우
	DRAWN	CHECK 1		APPR

ISSUES & REVISIONS

DRAWING TITLE
지상11,12층 평면도

DRAWN	한만수	SCALE	A1 : 150 A3 : 300
CHECK 1	김경훈		
CHECK 2	김영관	DATE	2013.11.
APPROVAL	이강우		

DRAWING NO.
A3-13