
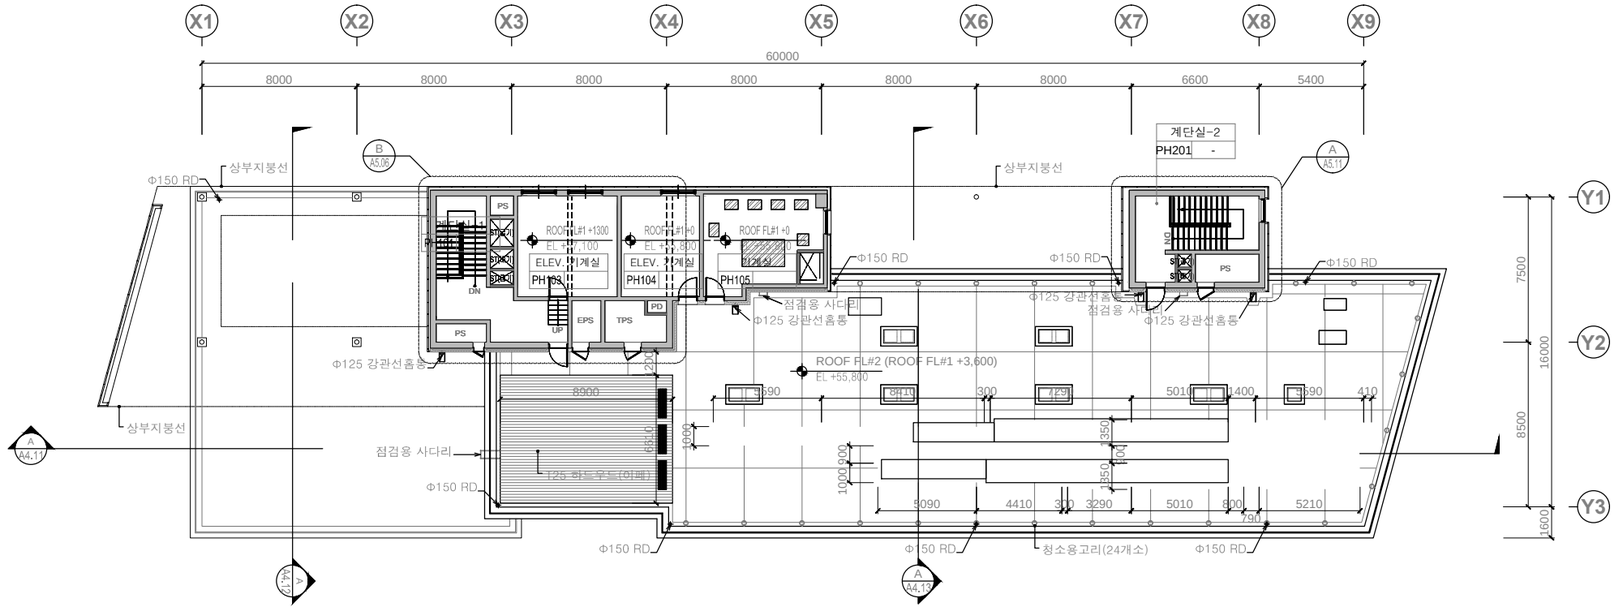


A 경상대 옥탑층 평면도
SCALE: 1/300

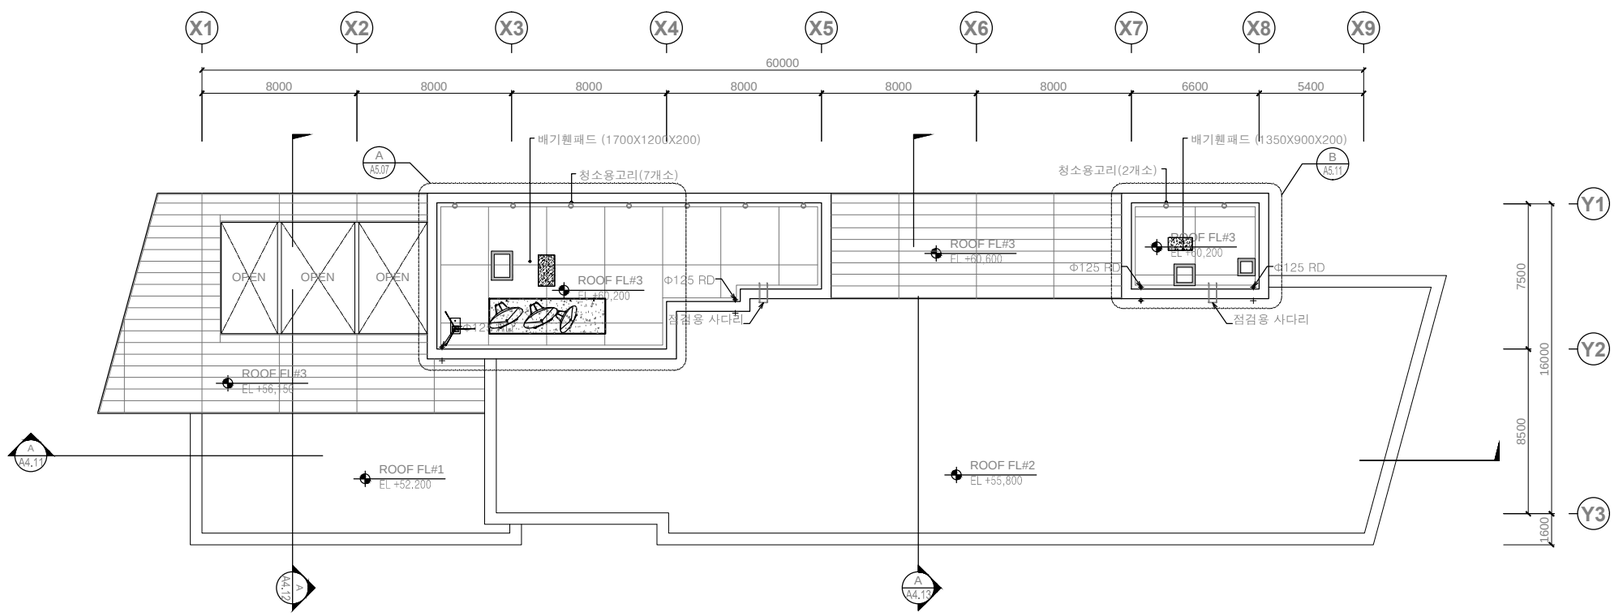

B 경상대 옥탑지붕 평면도
SCALE: 1/300

CLIENT
USW 수원대학교 THE UNIVERSITY OF SUWON

ARCHITECT
Chang-jo ARCHITECTS
(주)창조종합건축사사무소
826-26, Yeoksam-Dong,
Gangnam-Gu,Seoul,Korea 135-935
TEL. (82-2)2177-8300

PROJECT NO.
75241

PROJECT TITLE
수원대학교 경상대학 COMPLEX 증축설계

NOTE
1. R00F #1 FL±0 = EL+52,200 = G.L+123.20
2. ROOF #2 FL±0 = EL+54,500 = G.L+125.50
3. ROOF #3 FL±0 = EL+56,400 = G.L+127.40
4. ROOF #3 FL±0 = EL+57,000 = G.L+128.00

장비패드(H=200)

5. 데크하부는 기존 건축공사와 동일

*철골구조에 내화뿜칠 또는 내화페인트 적용기준: 2시간

㉮	완 강 기
	옥내 소화전함
	방수기구함

NO.	DESCRIPTION			DATE
1	설계변경 수정사항			2015.06.30
	정현돈	최현	김경훈	이강우
	DRAWN	CHECK 1		APPR

ISSUES & REVISIONS

DRAWING TITLE
옥탑1~2

DRAWN	한만수	SCALE	A1 : 150 A3 : 300
CHECK 1	김경훈		
CHECK 2	김영관	DATE	2013.11.
APPROVAL	이강우		

DRAWING NO.
A3-15